製品マーク	2-BK-13	製品台数	7
部材マーク	部　材	長さ(mm)	台数
2-GPz-1	PL12*230	375	7
2-RPz-19	PL9*213	355	7
2-RPz-24	PL9*142	350	1

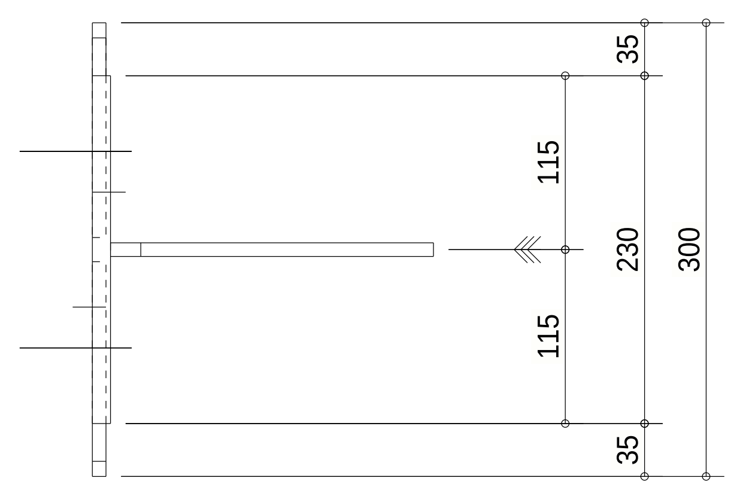
35
115
230
300
115
35

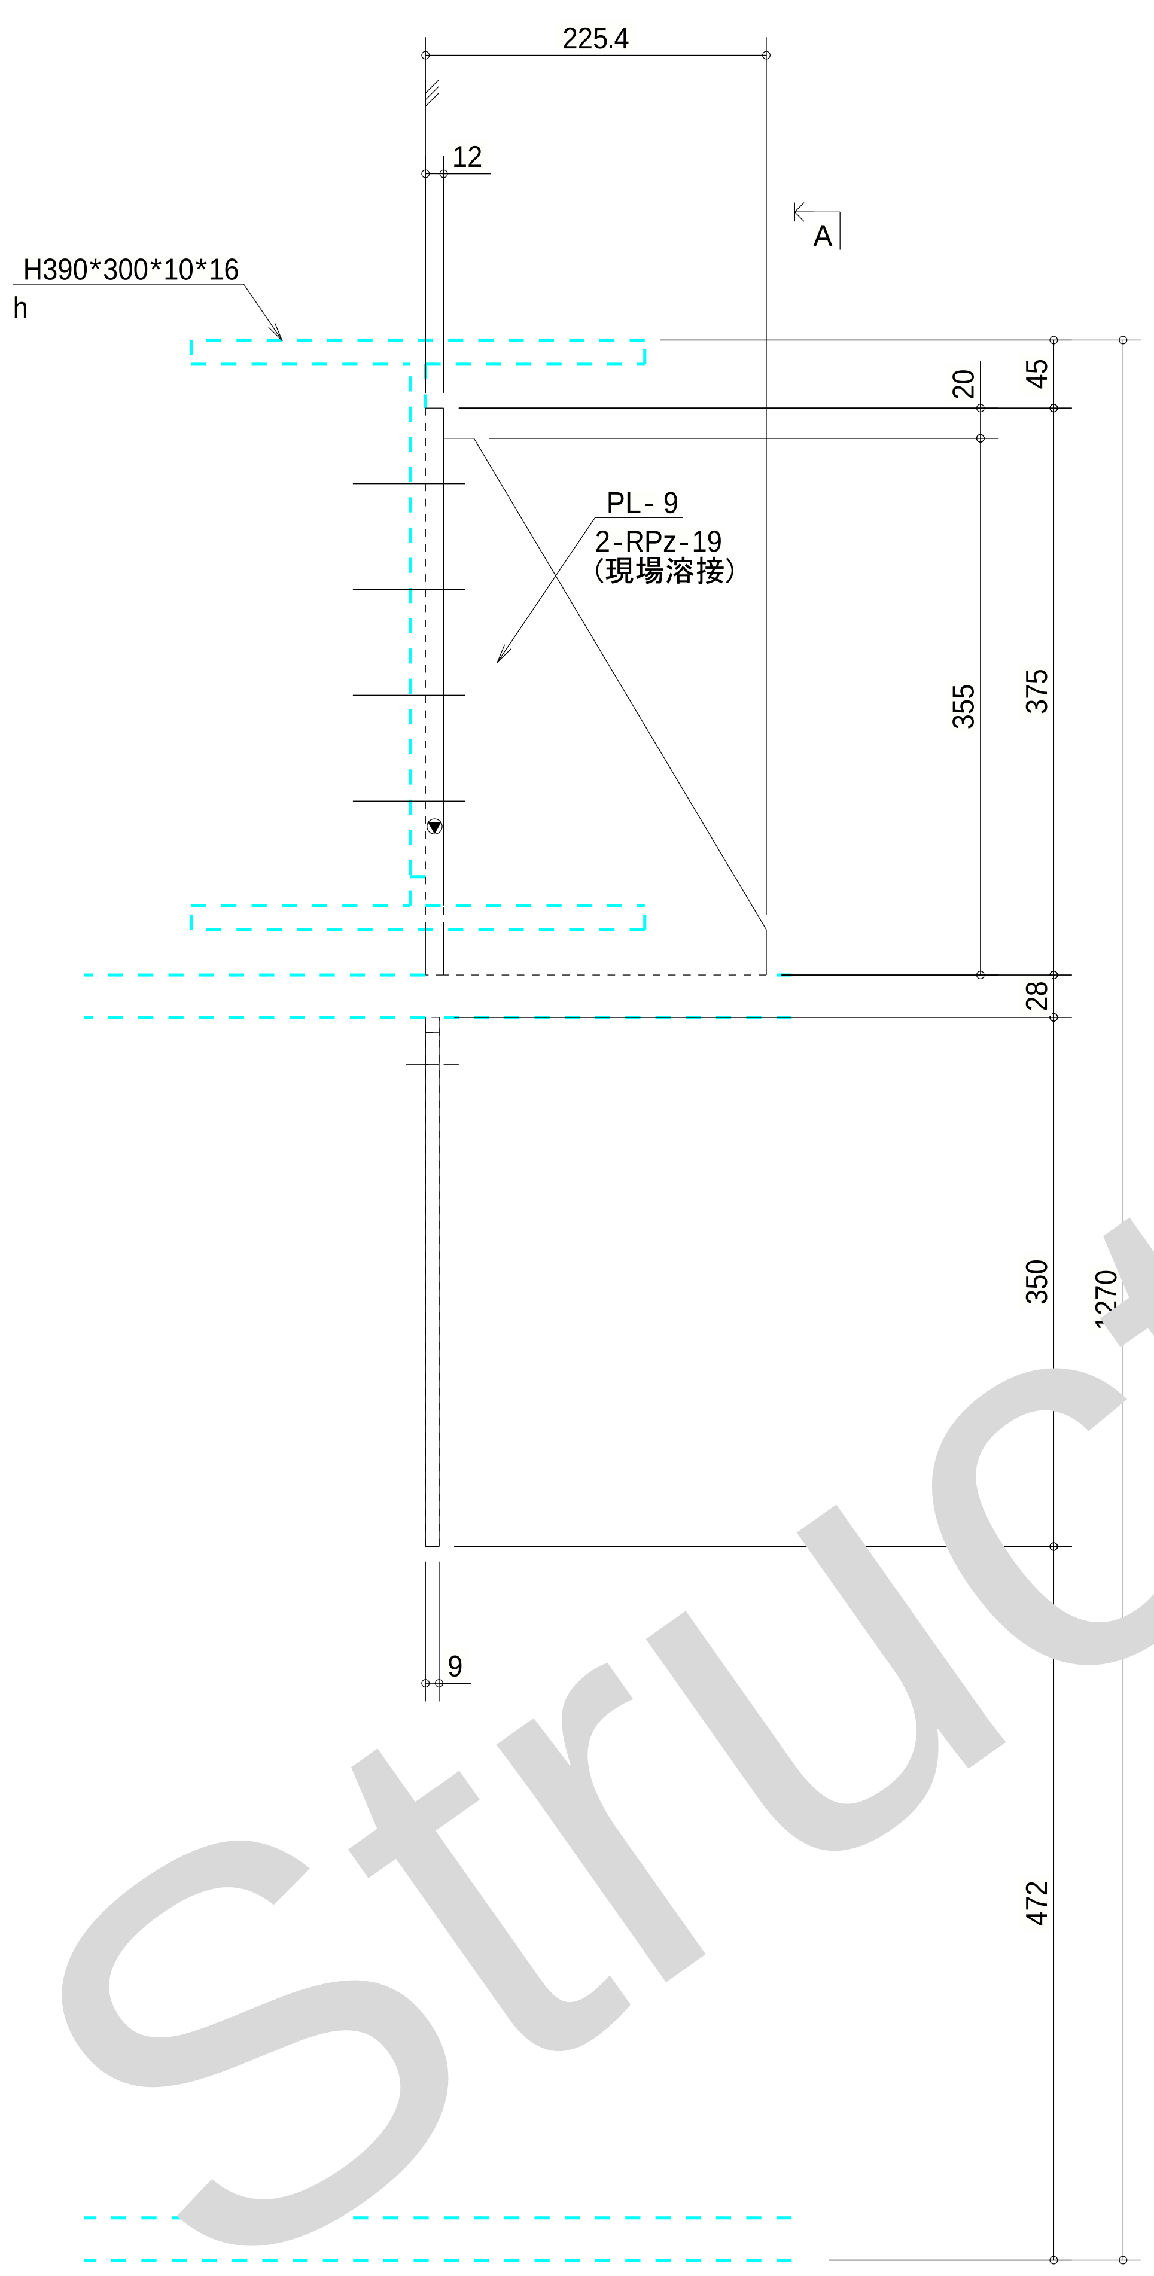
225.4
12
A
H390*300*10*16
h
PL- 9
2-RPz-19
（現場溶接）
20
45
355
375
28
350
1270
472
9

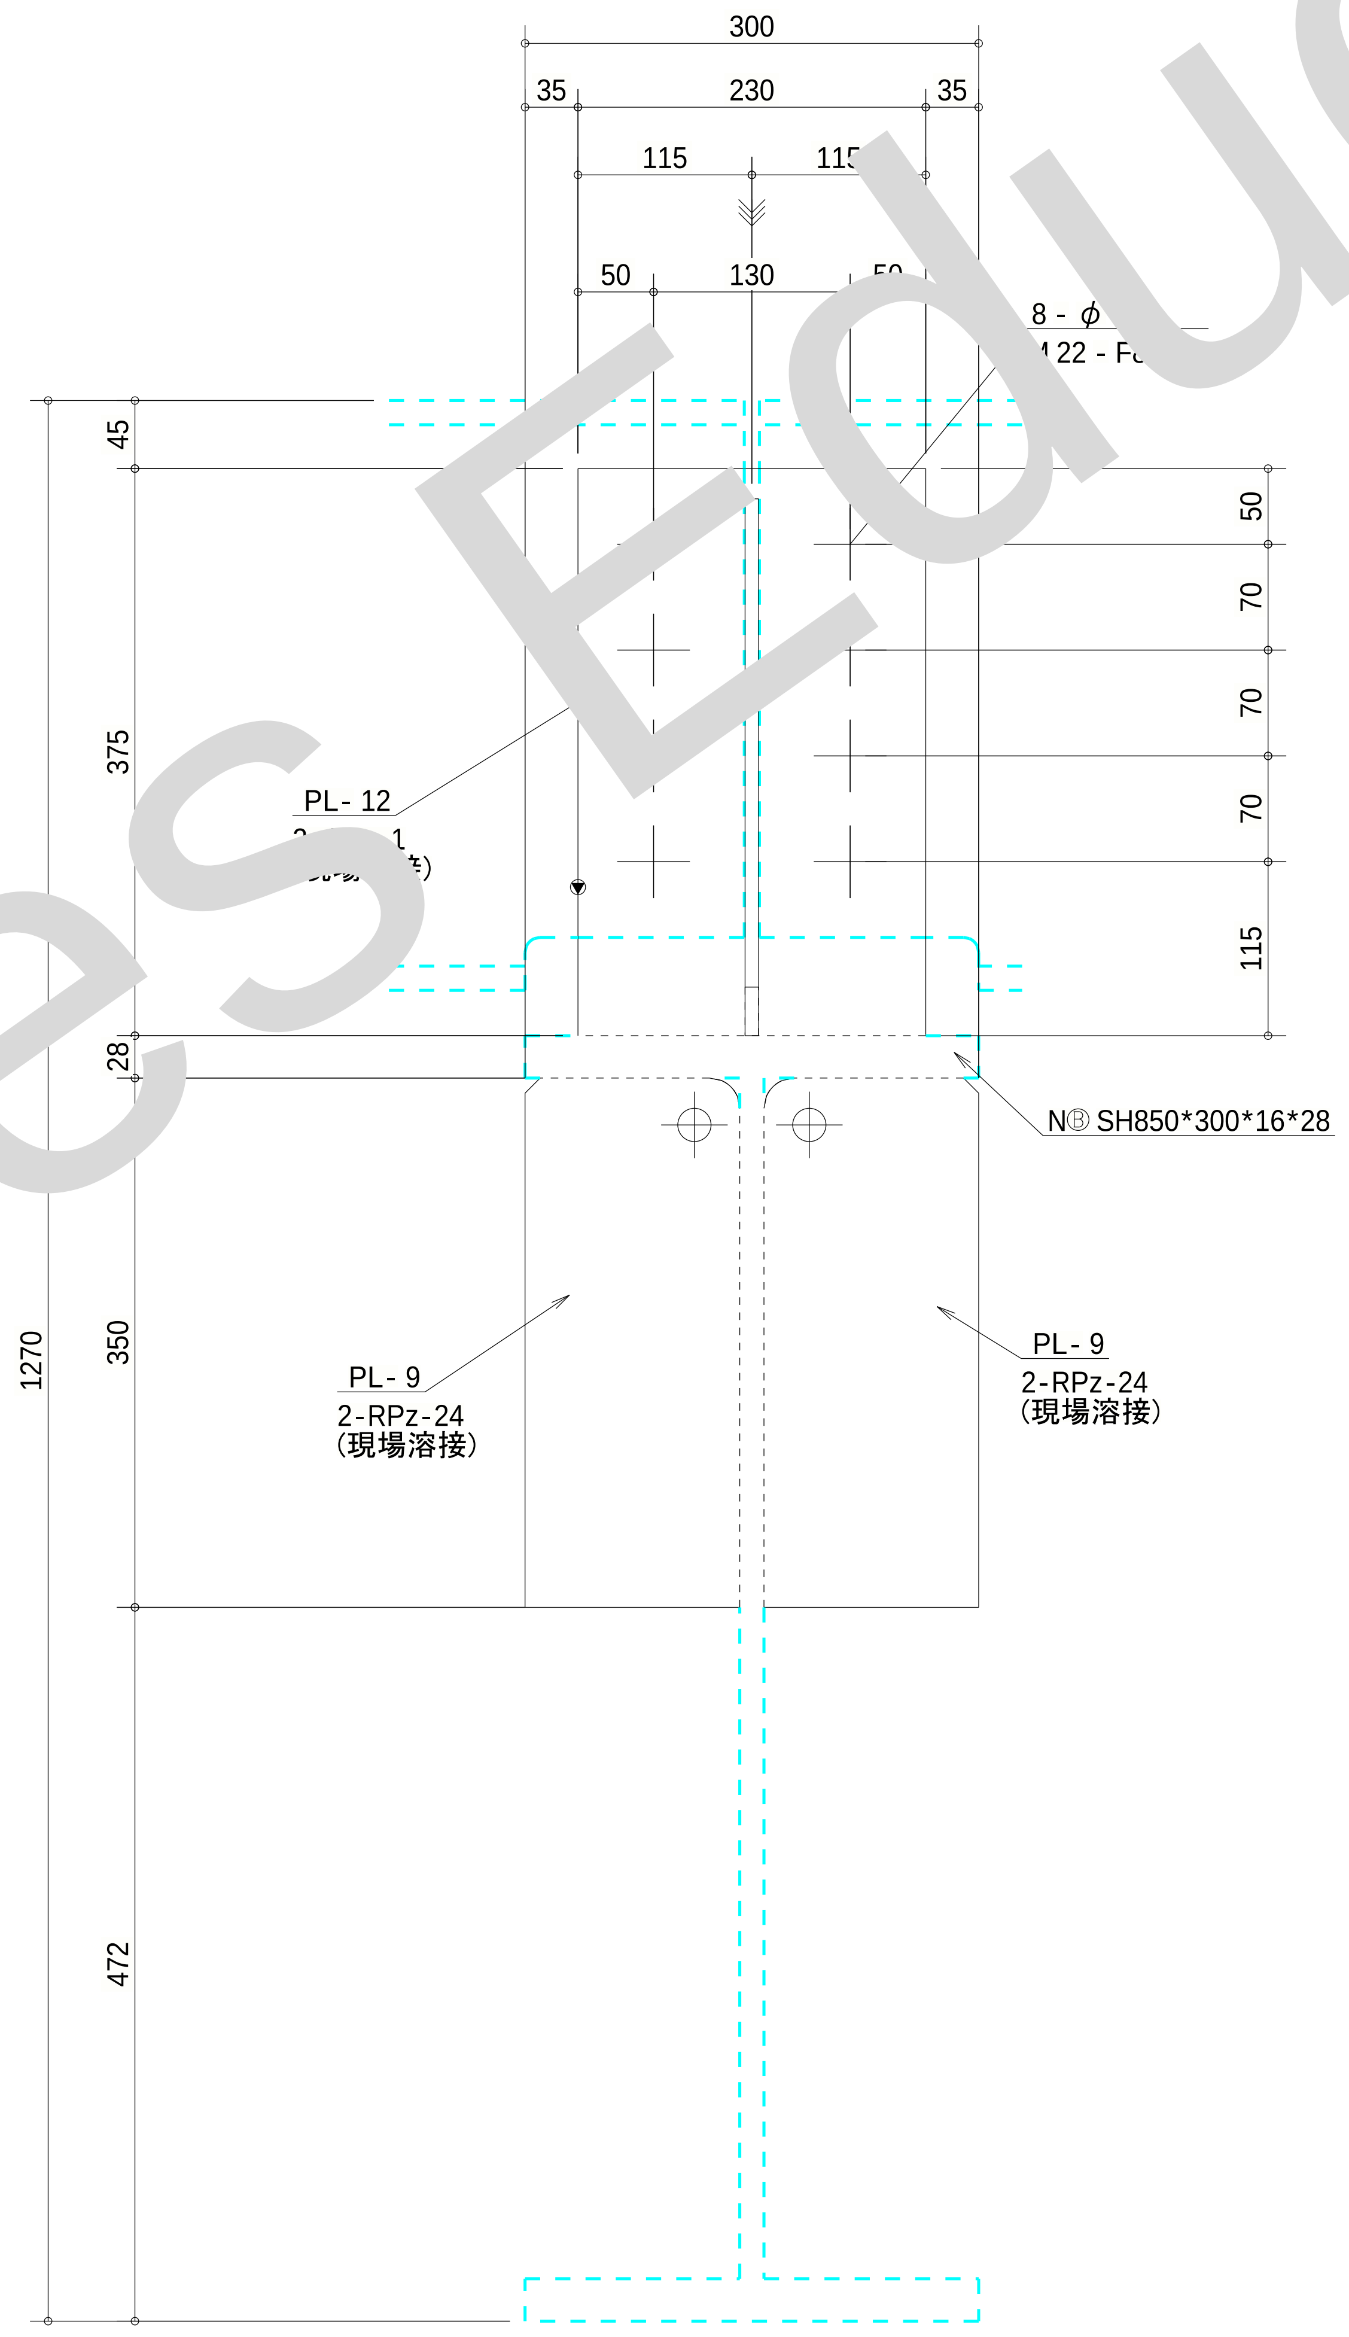
300
35
230
35
115
115
50
130
50
8 - φ
22 - F
PL- 12
45
375
28
350
1270
472
50
70
70
70
115
NⒷ SH850*300*16*28
PL- 9
2-RPz-24
（現場溶接）
PL- 9
2-RPz-24
（現場溶接）

A - A

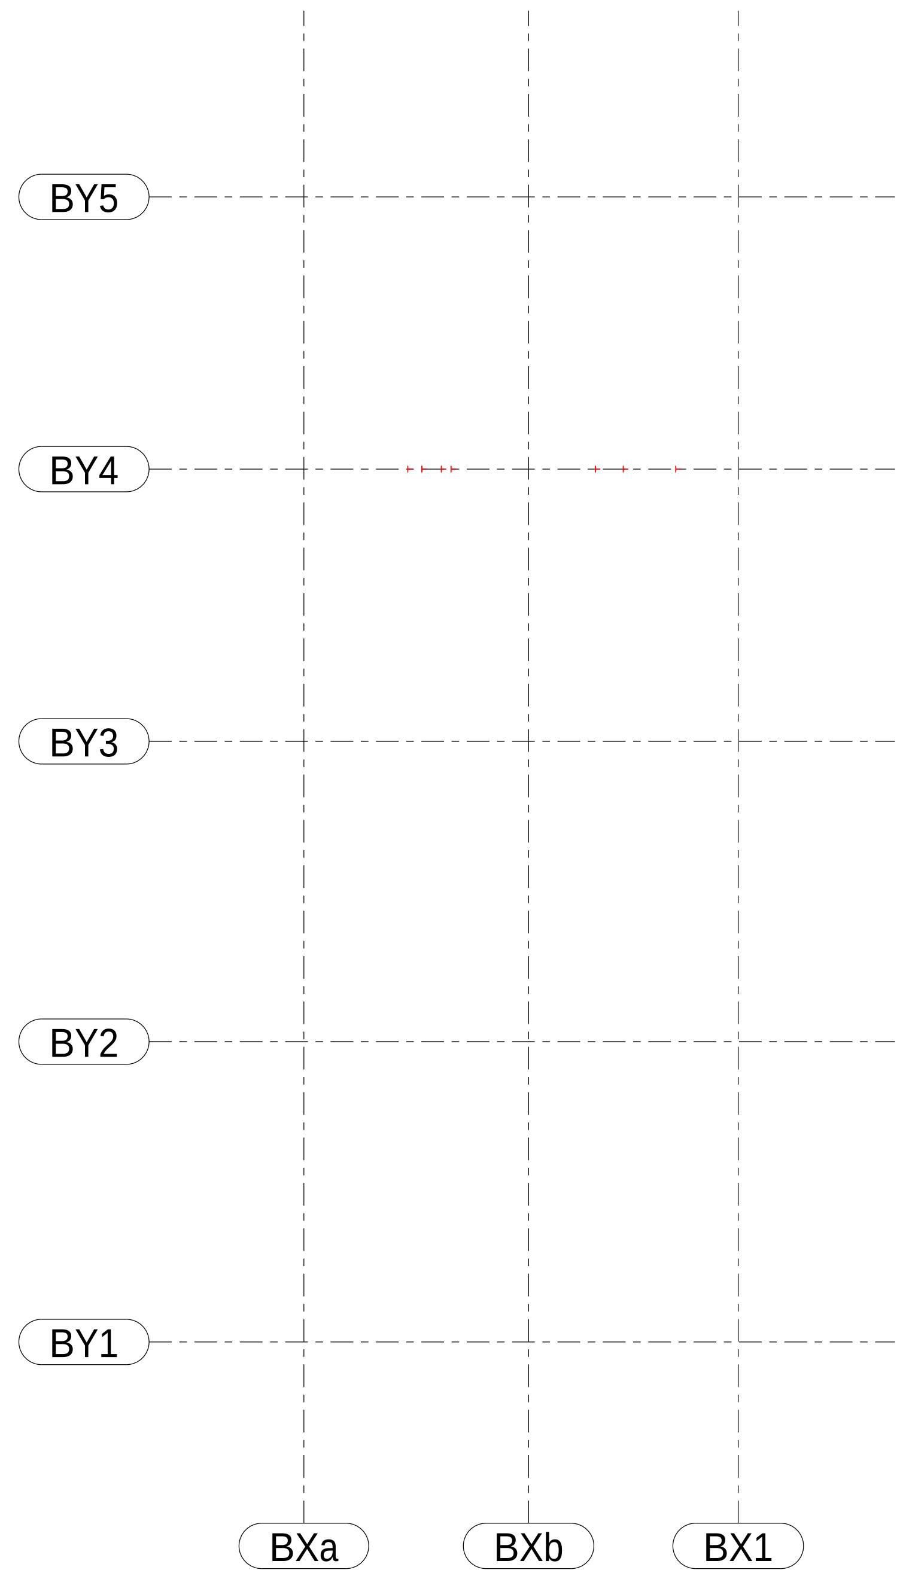
BY5
BY4
BY3
BY2
BY1
BXa
BXb
BX1

2-BK-13	PLATE	PL12*230	SS400	7　台

0 2026年06月29日. FOR APPROVAL

M12		
M16		
M20		
M22		
M24		

SS400		SM490A	○	BCP325B	P Ⓑ	TMCP325B	T Ⓑ
SN400B	N B	SN490B	N Ⓑ	BCP325C	P Ⓒ	TMCP325C	T Ⓒ
SN400C	N C	SN490C	N Ⓒ	BCP385B	P B	TMCP385B	T B
				BCP385C	P C	TMCP385C	T C
				BCR295	R □		

ＮＥＣファシリティーズ株式会社
株式会社織本構造設計

株式会社　大林組

(A1) 1:5
(A3) 1:10

26 . 07 . 16

株式会社　辻鉄商工

辻 | - | 梁 | -

TOK1_B_B210-B540

2PL-013

プレート 詳細図

27-011

2026年
07月16日

2026年
06月29日

Tekla Structures Educational